COURTYARD APARTMENTS

50 ft x 100 ft (15.24 m x 30.48 m) plot | Nairobi, Kenya | GF + L1-L4, 13 homes, 9 basement bays

KEY DATA

ITEM	VALUE
Plot	15.24 m x 30.48 m (50 x 100 ft)
Levels	B1, GF, L1, L2, L3, L4, roof
Homes	13 (1 GF + 3 per upper floor)
Parking	9 bays incl. 1 accessible, 1 EV
Courtyard	112.1 m2 open to sky
GF FFL	+0.90 m podium
Roof slab	+16.20 m; parapet +17.30 m
Code	Kenya National Building Code 2024 (LN 47/2024)

DRAWING REGISTER

S01 Cover, key plan, drawing register

S02 Basement floor plan B1 -2.00

S03 Ground floor plan GF +0.90


S04 Typical upper floor plan L1-L4

S05 Roof plan +16.20

S06 Sections A-A and B-B

S07 Elevations

S08 Schedules and compliance summary

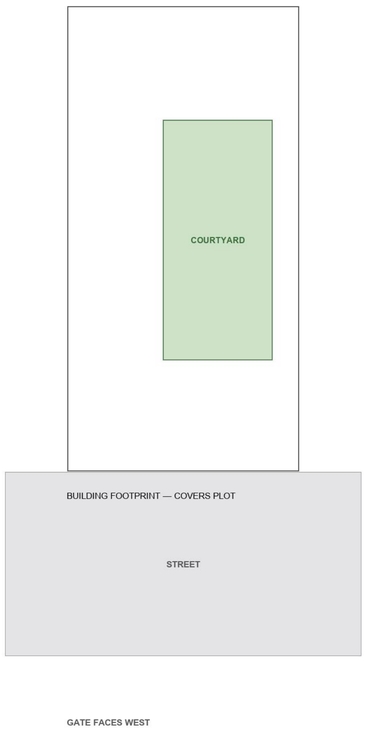

SCALE 1:200

0 2 4 6 8 10 m

N


REV P01

S01

PROJECT	**COURTYARD APARTMENTS — 50 x 100 ft PLOT, NAIROBI**
SHEET	**COVER / KEY PLAN**
SCALE	1:200
DATE	OCTOBER 2026
STATUS	FOR DEVELOPMENT CONTROL SUBMISSION
DRAWN / CHECKED	AV / —

BASEMENT FLOOR PLAN — B1 (-2.00)

Cut at -0.90 m (+1.10 m above FFL). Dimensions in metres. Do not scale from this drawing.

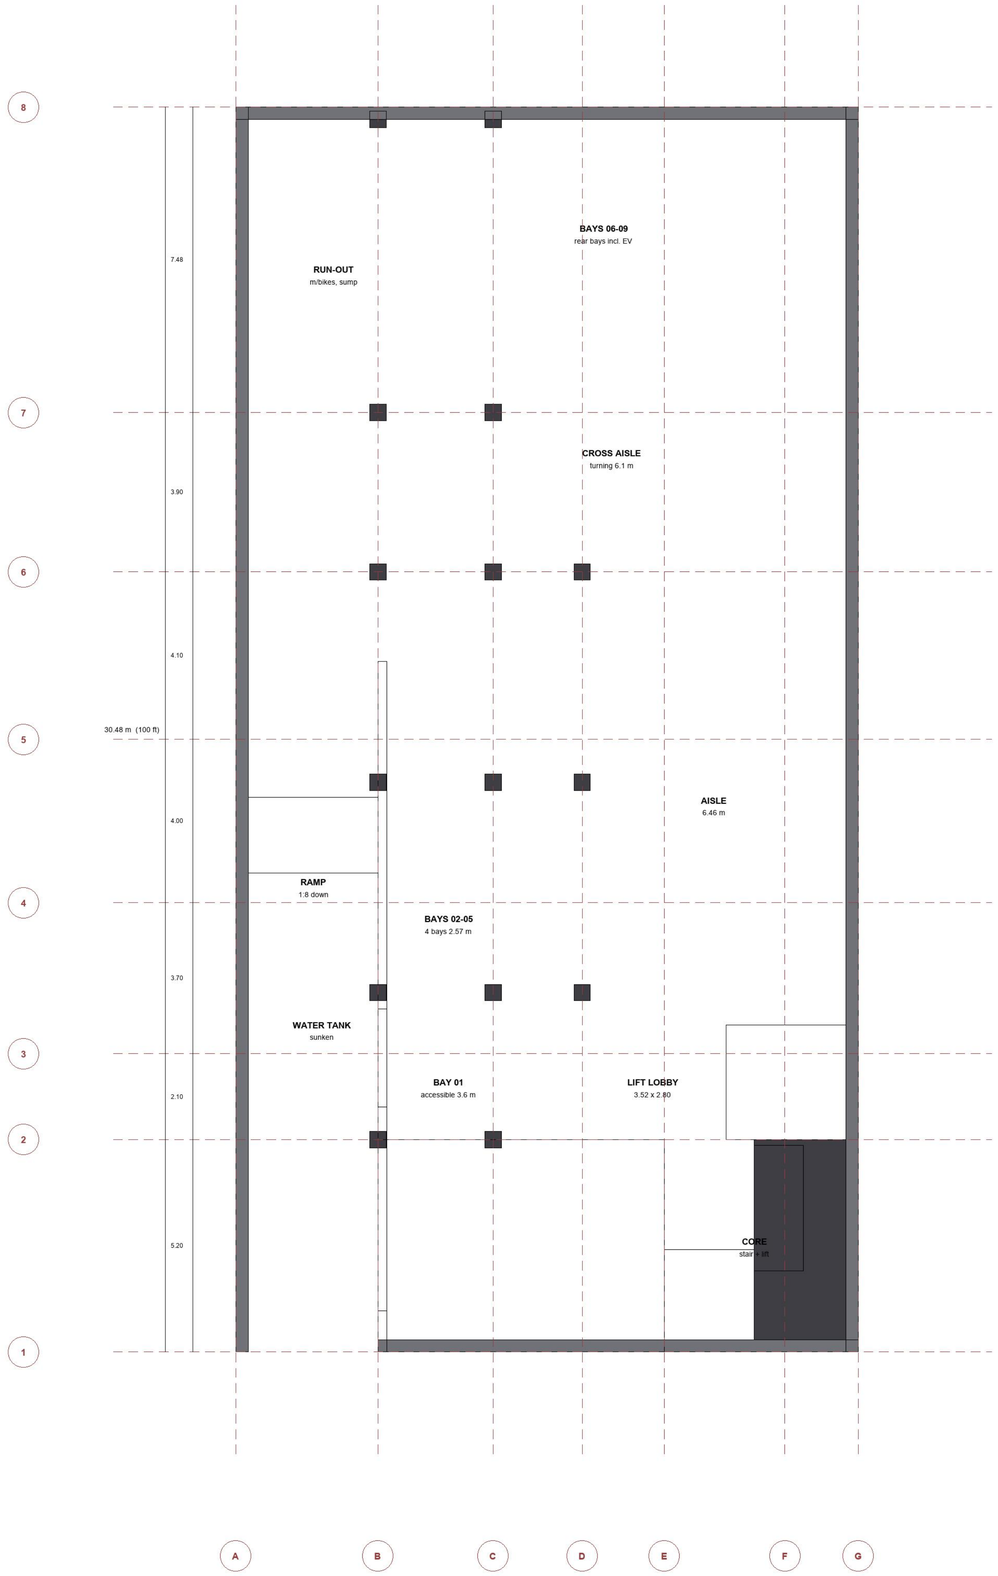

SCALE 1:75

0 2 4 6

N


REV P01

S02

PROJECT	**COURTYARD APARTMENTS — 50 x 100 ft PLOT, NAIROBI**
SHEET	**BASEMENT FLOOR PLAN — B1 (-2.00)**
SCALE	1:75
DATE	OCTOBER 2026
STATUS	FOR DEVELOPMENT CONTROL SUBMISSION
DRAWN / CHECKED	AV / —

GROUND FLOOR PLAN — GF (+0.90)

Cut at +2.00 m (+1.10 m above FFL). Dimensions in metres. Do not scale from this drawing.

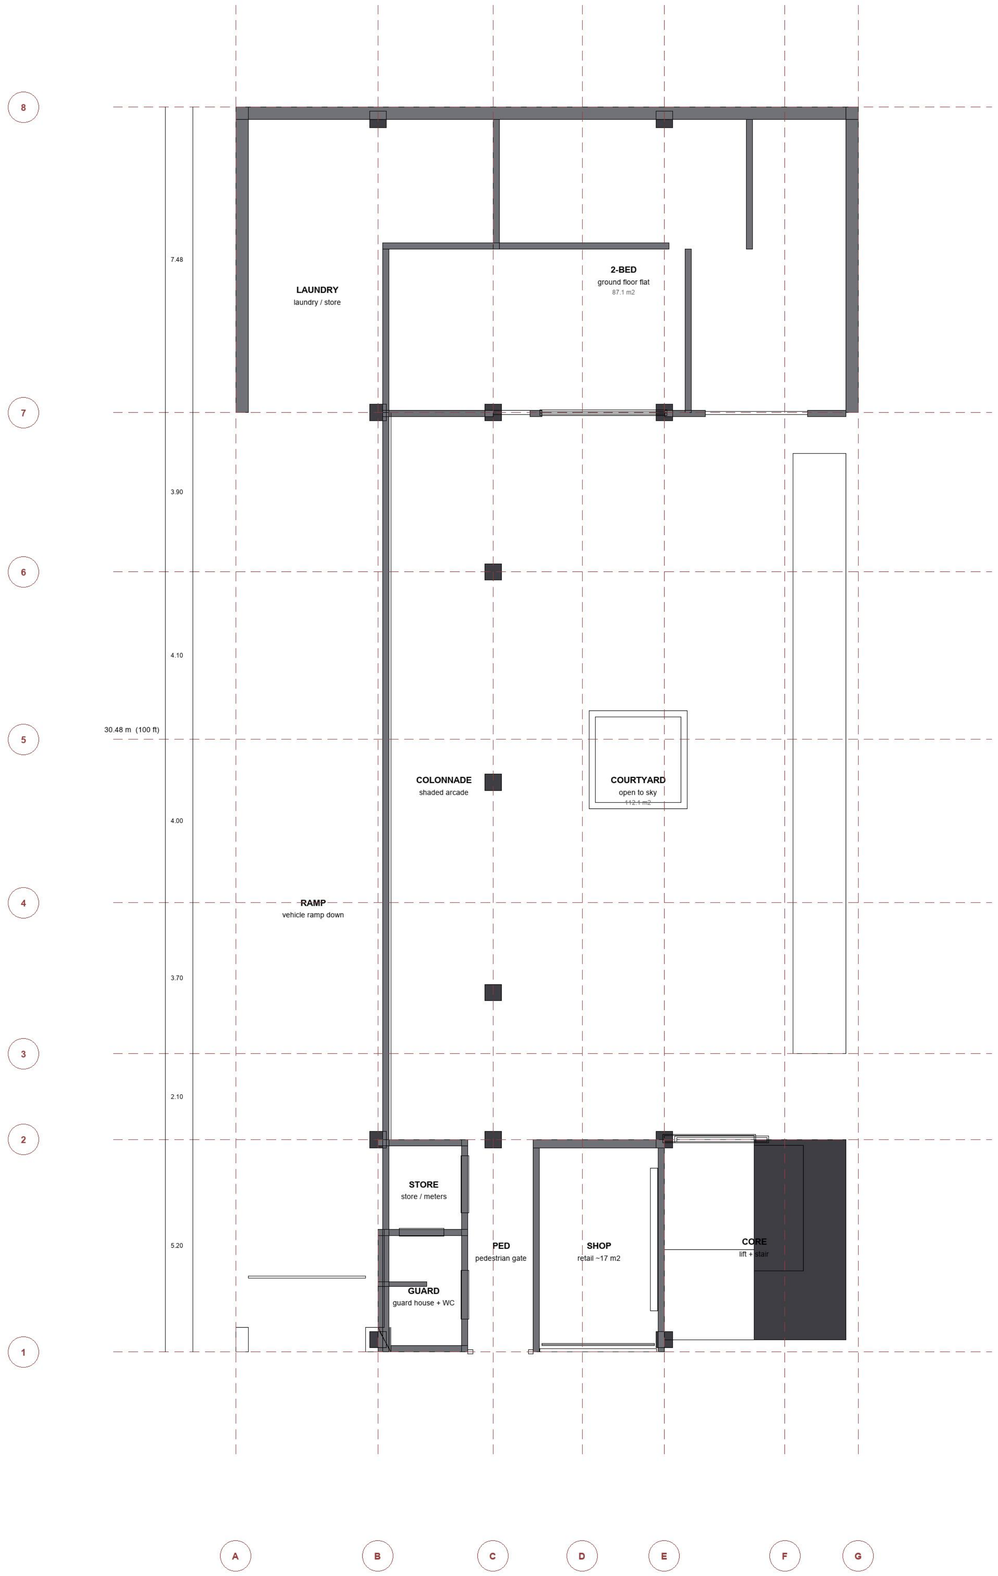

SCALE 1:75

0 2 4 6

N


REV P01

S03

PROJECT	**COURTYARD APARTMENTS — 50 x 100 ft PLOT, NAIROBI**
SHEET	**GROUND FLOOR PLAN — GF (+0.90)**
SCALE	1:75
DATE	OCTOBER 2026
STATUS	FOR DEVELOPMENT CONTROL SUBMISSION
DRAWN / CHECKED	AV / —

TYPICAL UPPER FLOOR PLAN — L1-L4

Cut at +5.30 m (+1.10 m above FFL). Dimensions in metres. Do not scale from this drawing.

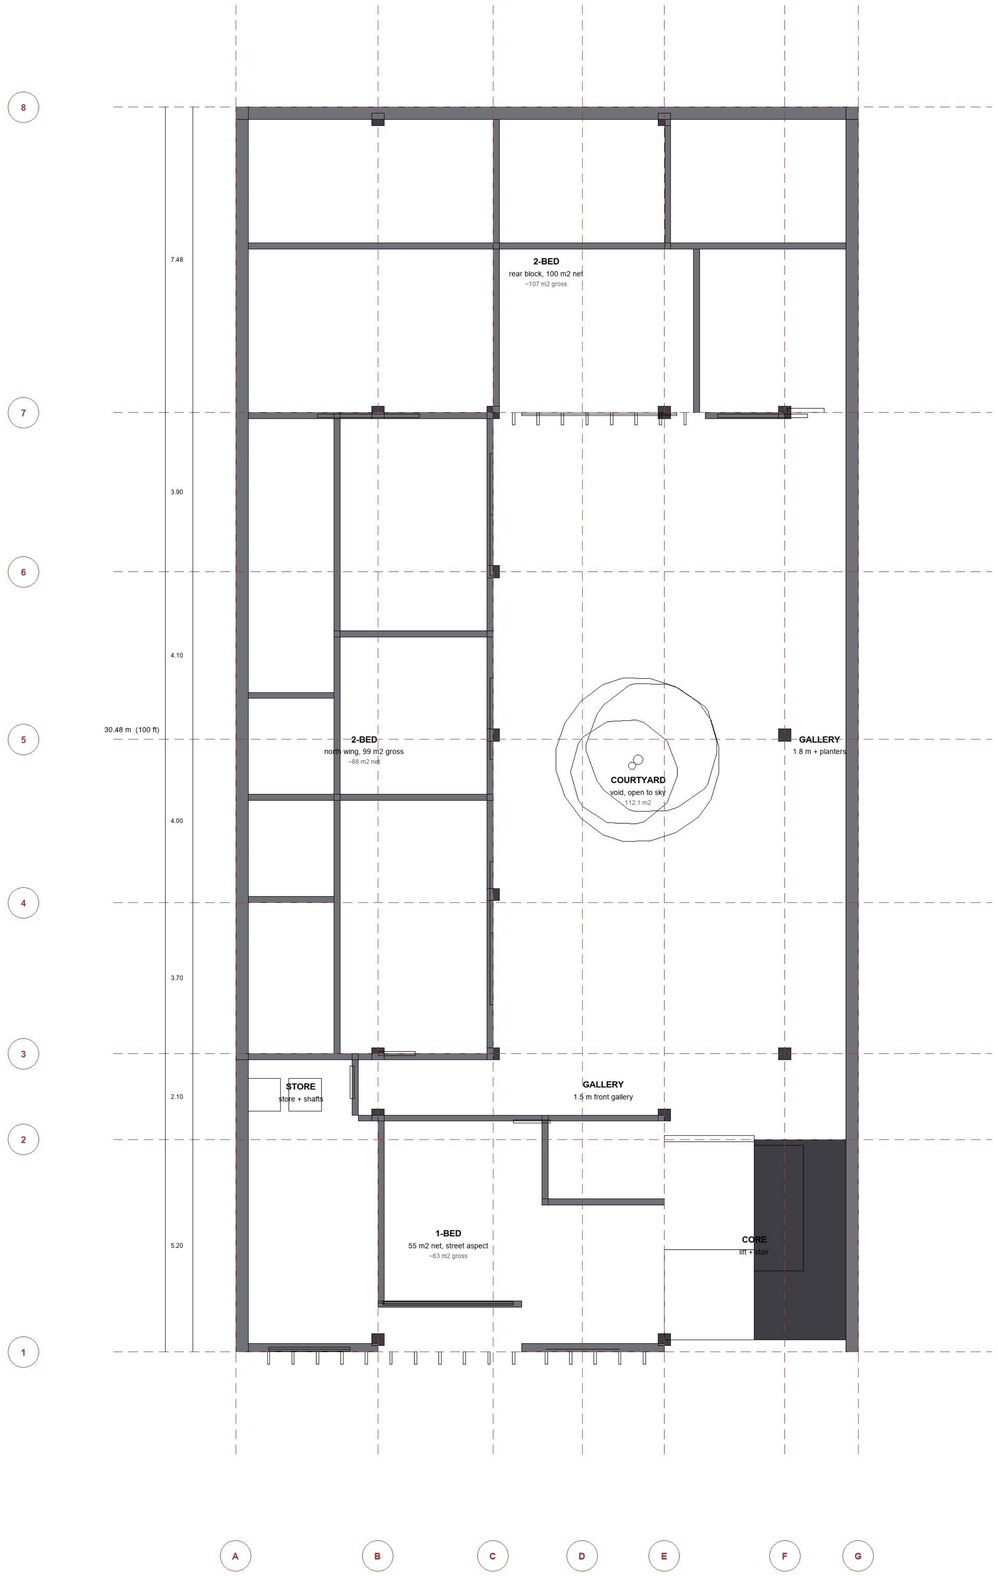

SCALE 1:75

0 2 4 6

N


REV P01

S04

PROJECT	**COURTYARD APARTMENTS — 50 x 100 ft PLOT, NAIROBI**
SHEET	**TYPICAL UPPER FLOOR PLAN — L1-L4**
SCALE	1:75
DATE	OCTOBER 2026
STATUS	FOR DEVELOPMENT CONTROL SUBMISSION
DRAWN / CHECKED	AV / —

ROOF PLAN — +16.20

Cut at +17.30 m (+1.10 m above FFL). Dimensions in metres. Do not scale from this drawing.

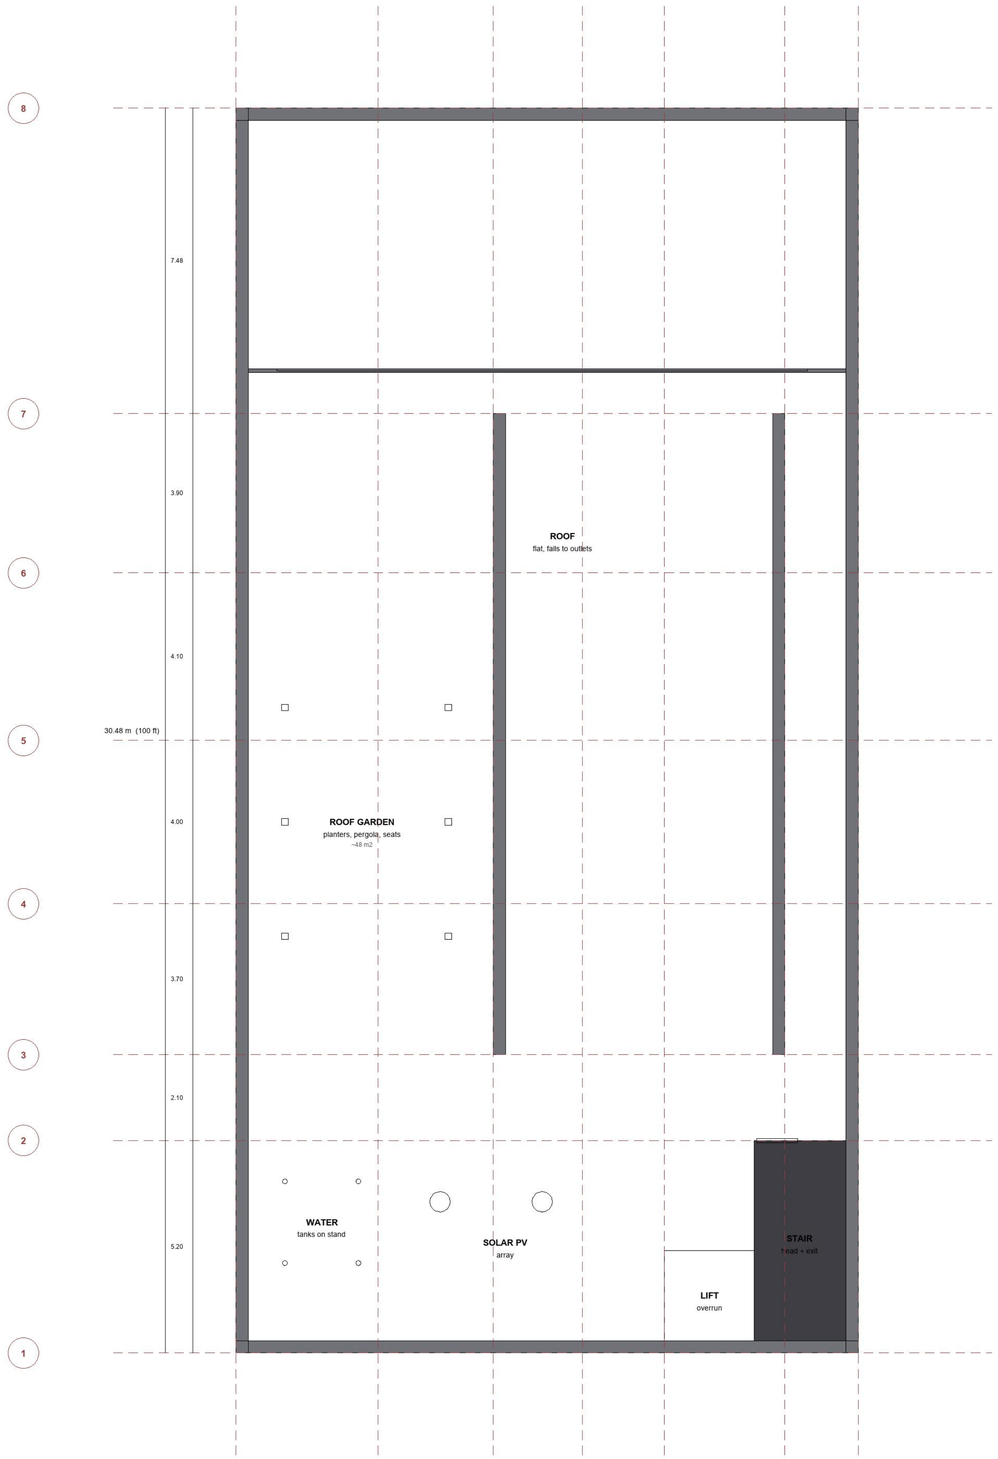

SCALE 1:75


0 2 4 6

N


REV P01

S05

PROJECT	**COURTYARD APARTMENTS — 50 x 100 ft PLOT, NAIROBI**
SHEET	**ROOF PLAN — +16.20**
SCALE	1:75
DATE	OCTOBER 2026
STATUS	FOR DEVELOPMENT CONTROL SUBMISSION
DRAWN / CHECKED	AV / —

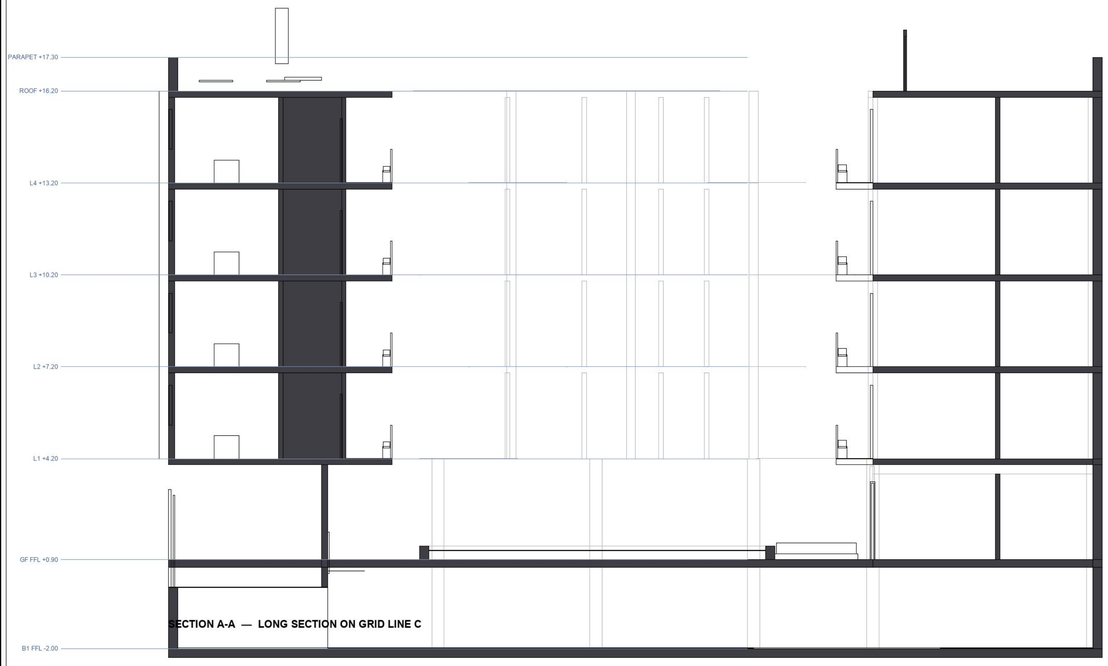

SECTION A-A — LONG SECTION ON GRID LINE C

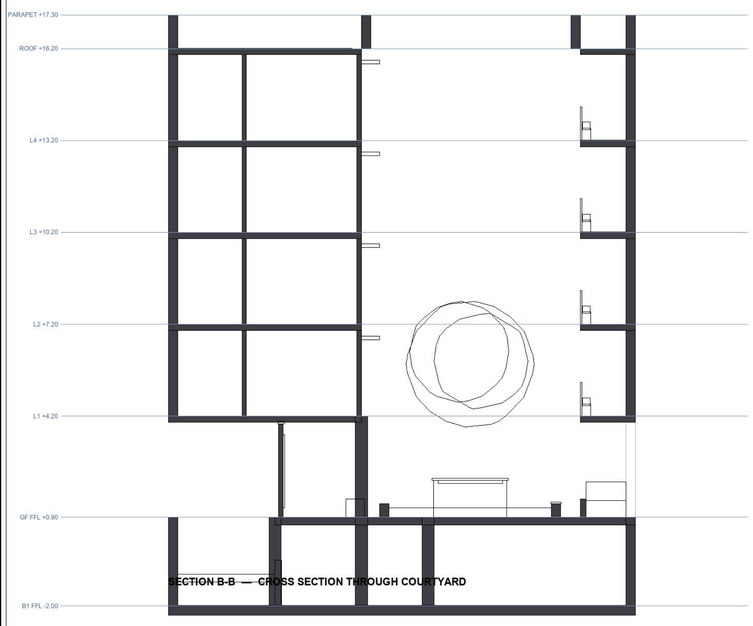

SECTION B-B — CROSS SECTION THROUGH COURTYARD

SCALE 1:100

0 2 4 6 8 10 m


N

REV P01


S06

PROJECT	**COURTYARD APARTMENTS — 50 x 100 ft PLOT, NAIROBI**
SHEET	**SECTIONS**
SCALE	1:100
DATE	OCTOBER 2026
STATUS	FOR DEVELOPMENT CONTROL SUBMISSION
DRAWN / CHECKED	AV / —


Side elevations abut the boundary walls and carry no windows (design brief); they are shown for completeness.

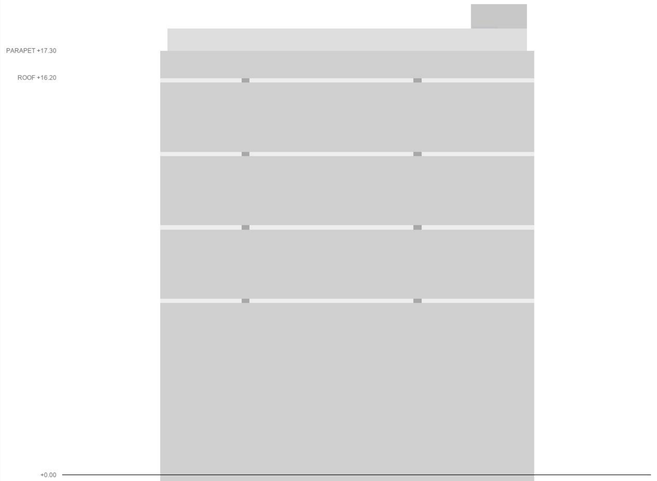


EAST ELEVATION — REAR

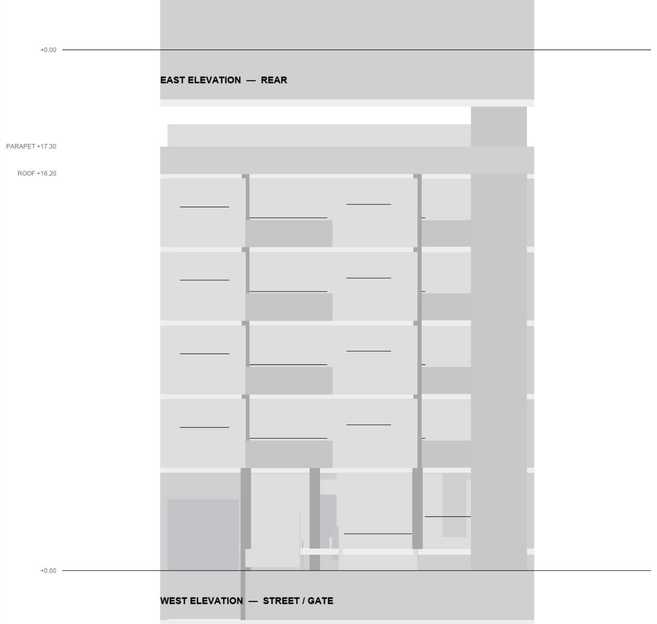

WEST ELEVATION — STREET / GATE

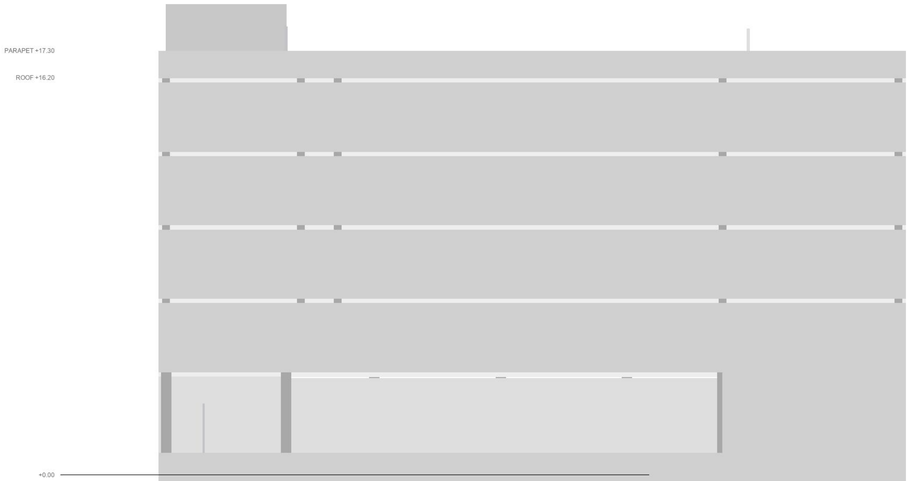

SOUTH ELEVATION

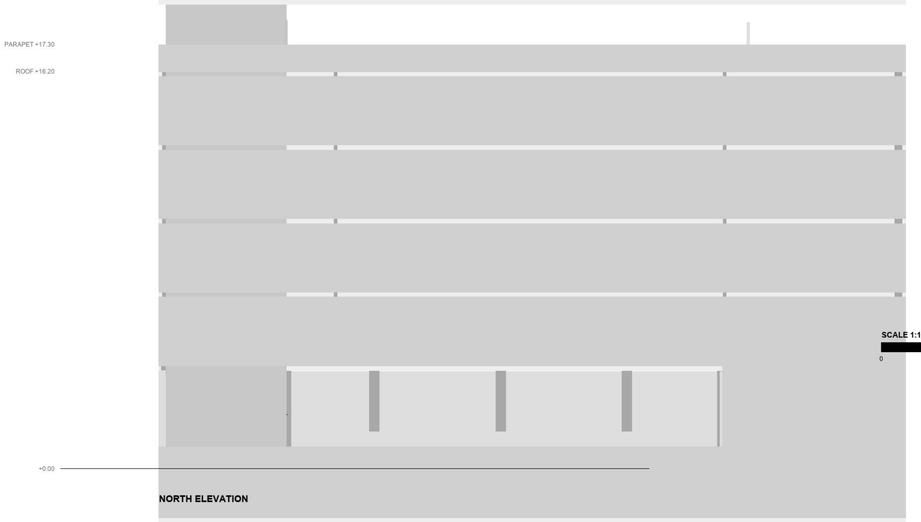

NORTH ELEVATION

SCALE 1:125

0 2 4 6 8 10 m

N

REV P01

S07

PROJECT	**COURTYARD APARTMENTS — 50 x 100 ft PLOT, NAIROBI**
SHEET	**ELEVATIONS**
SCALE	1:125
DATE	OCTOBER 2026
STATUS	FOR DEVELOPMENT CONTROL SUBMISSION
DRAWN / CHECKED	AV / —

AREA SCHEDULE

ELEMENT / LEVEL	QUANTITY	AREA
B1 Basement parking	9 bays + bikes	464.5 m2 gross
GF Commercial shop	1 unit	16.7 m2
GF Guard house + WC	1	6.6 m2
GF Shaded colonnade	-	48.1 m2
GF 2-bed flat	1 unit	87.1 m2
GF Courtyard, open to sky	-	112.1 m2
L1-L4 1-bed (front)	4 units	~63 m2 each
L1-L4 2-bed (north wing)	4 units	~99 m2 each
L1-L4 2-bed (rear, premium)	4 units	~107 m2 each
Roof garden terrace	pergola, planters, seats	57.0 m2
Roof slab (excl. terrace fit-out)	-	327.7 m2

ROOM SCHEDULE — TYPICAL

UNIT	ROOM	SIZE
Type A 1-bed	living/kitchenette	20-24 m2
Type A 1-bed	bedroom	>=3.0 x 3.6 m
Type A 1-bed	bathroom	~1.8 x 2.2 m
Type B 2-bed	living / dining	20-26 m2
Type B 2-bed	kitchen + drying	7-9 m2
Type B 2-bed	master + en-suite	>=3.3 x 3.6 + 1.8 x 2.4 m
Type B 2-bed	bedroom 2	>=3.0 x 3.3 m
Type B 2-bed	common bath / linen	1.8 x 2.2 m / store

COMPLIANCE SUMMARY

s.17 balustrades >= 1.0 m	1.10 m	**PASS**
s.20 courtyard >= 35 m2, min dim 4.5 m	112.1 m2 / 7.14 m	**PASS**
s.21 <= 5 storeys, single stair + ramp	5 storeys	**PASS**
s.38 EV bays >= 5%	1 of 9 = 11.1%	**PASS**
s.41 vehicle barriers 375-610 mm	450 mm kerb	**PASS**
s.42 <= 1:25 within 5 m of road	4.0%	**PASS**
s.44 ramp <= 12.5%, width >= 3.0 m	12.5%, 3.18 m	**PASS**
s.129 external walls >= 200 mm	200 mm stone + 300 RC	**PASS**
s.137 zone of space >= H/3	7.14 m >= 4.40 m	**PASS**
s.143(1) windows >= 10% floor area	7.2% modelled - see note	**CHECK**
s.143(2) glazing + balcony uplift >= 30%	not verified	**CHECK**
s.194(2) stair continues to roof	to +19.00 m	**PASS**
s.205 risers 150-180, treads 250-320	176 / 280 mm	**PASS**
s.353 accessible bay 3.6 m by lift	Bay 01	**PASS**
s.400 basement 2 escape routes	stair + ramp	**PASS**
s.18 6 m open front space	shop on boundary	**CONFLICT**
s.19 1.5 m open side space	walls both sides	**CONFLICT**

NOTES

1. GFA: 1,357 m2 on the basis of enclosed floor area, excluding the courtyard void, the open colonnade and the open access galleries. Including every slab plate the measured figure is 1,670.7 m2 above ground (2,135 m2 with B1).
2. s.143(1): the model contains 28 glazing panels totalling 119.5 m2, which is 7.2% of the floor plate - below the 10% required. The spec's window schedule lists 119 windows, so the model is probably incomplete rather than the design failing. Both must be reconciled before submission.
3. The saved model has no openings cut in the host walls; the drawings cut them at render time. See Model QA & Render Notes.

N

REV P01

S08

PROJECT	**COURTYARD APARTMENTS — 50 x 100 ft PLOT, NAIROBI**
SHEET	**SCHEDULES & COMPLIANCE**
SCALE	NTS
DATE	OCTOBER 2026
STATUS	FOR DEVELOPMENT CONTROL SUBMISSION
DRAWN / CHECKED	AV / —